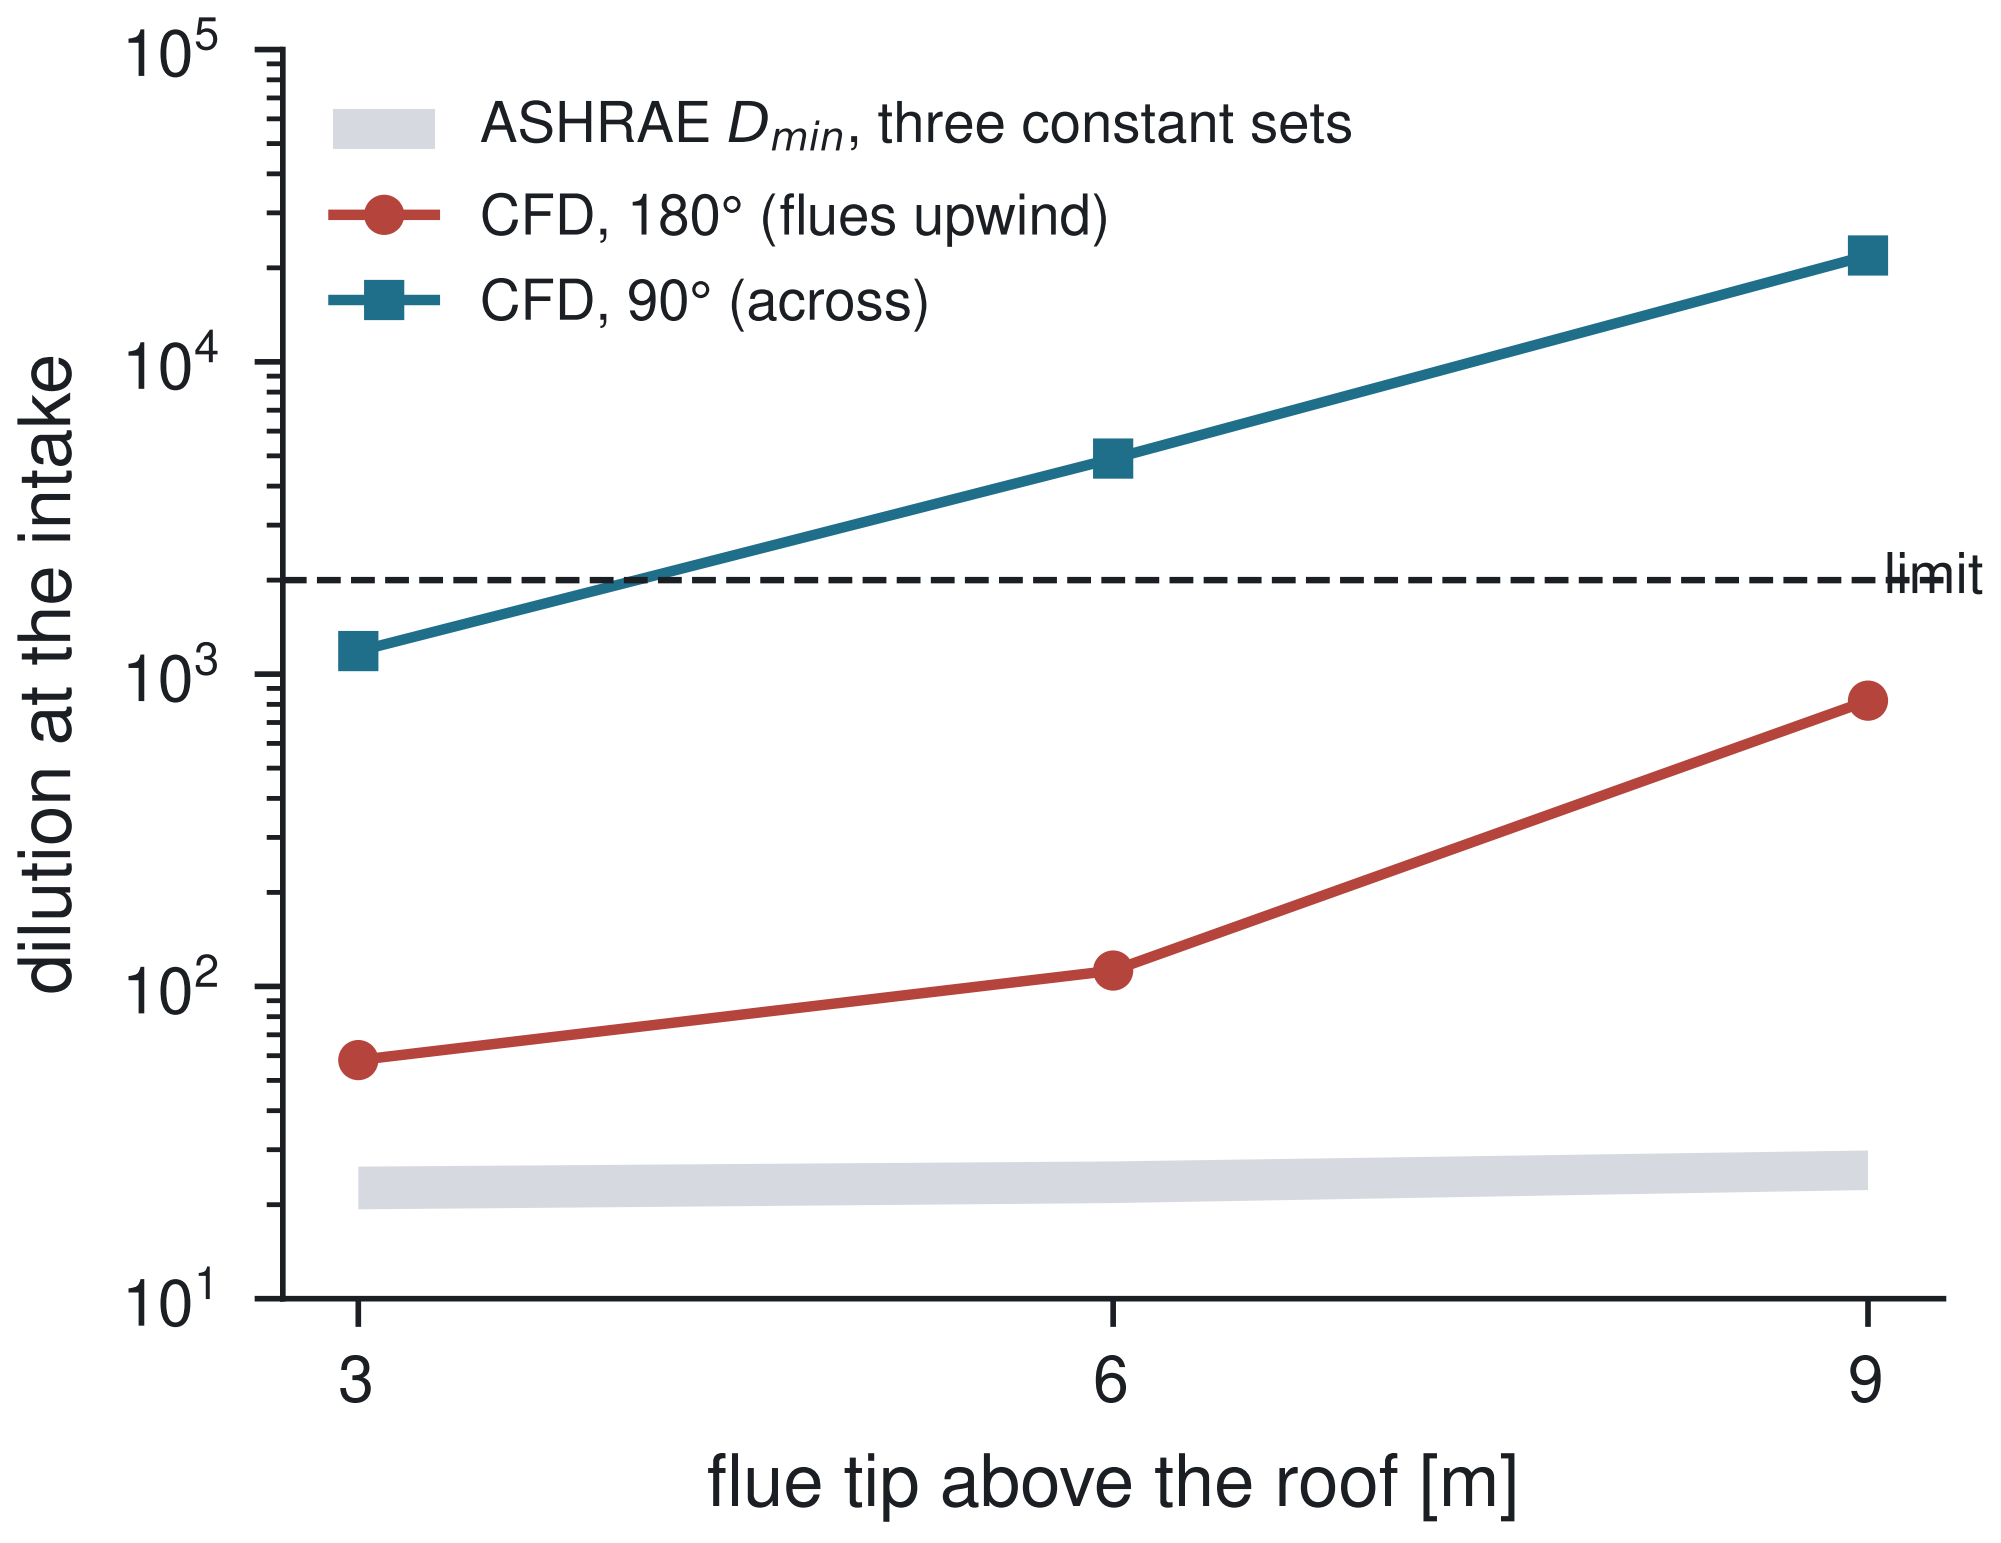
ASHRAE D_{min}, three constant sets
CFD, 180° (flues upwind)
CFD, 90° (across)
limit
dilution at the intake
10^5
10^4
10^3
10^2
10^1
3
6
9
flue tip above the roof [m]